

ÉÉNLIJNSCHEMA 10 kV – BESS-STATION FUDURA, AANSLUITING OP GETEC HSS RAIL C

Concept / voorstel – vervolg op Getec-tekening A0-0.673.581 (Hoogsp. inst. 10 kV). Nieuw = oranje. Bestaand Getec = zwart.

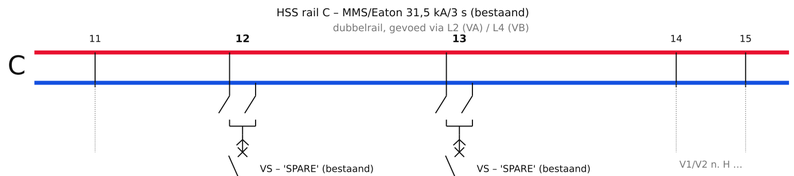

! Velden C12 en C13 altijd op DEZELFDE rail (VA- of VB-zijde) schakelen.
Gesloten lus via twee verschillende rails overbrugt de smoorspoelen L2/L4 en de Is-begrenzer → kortsluitstroom en lusstromen nemen toe.

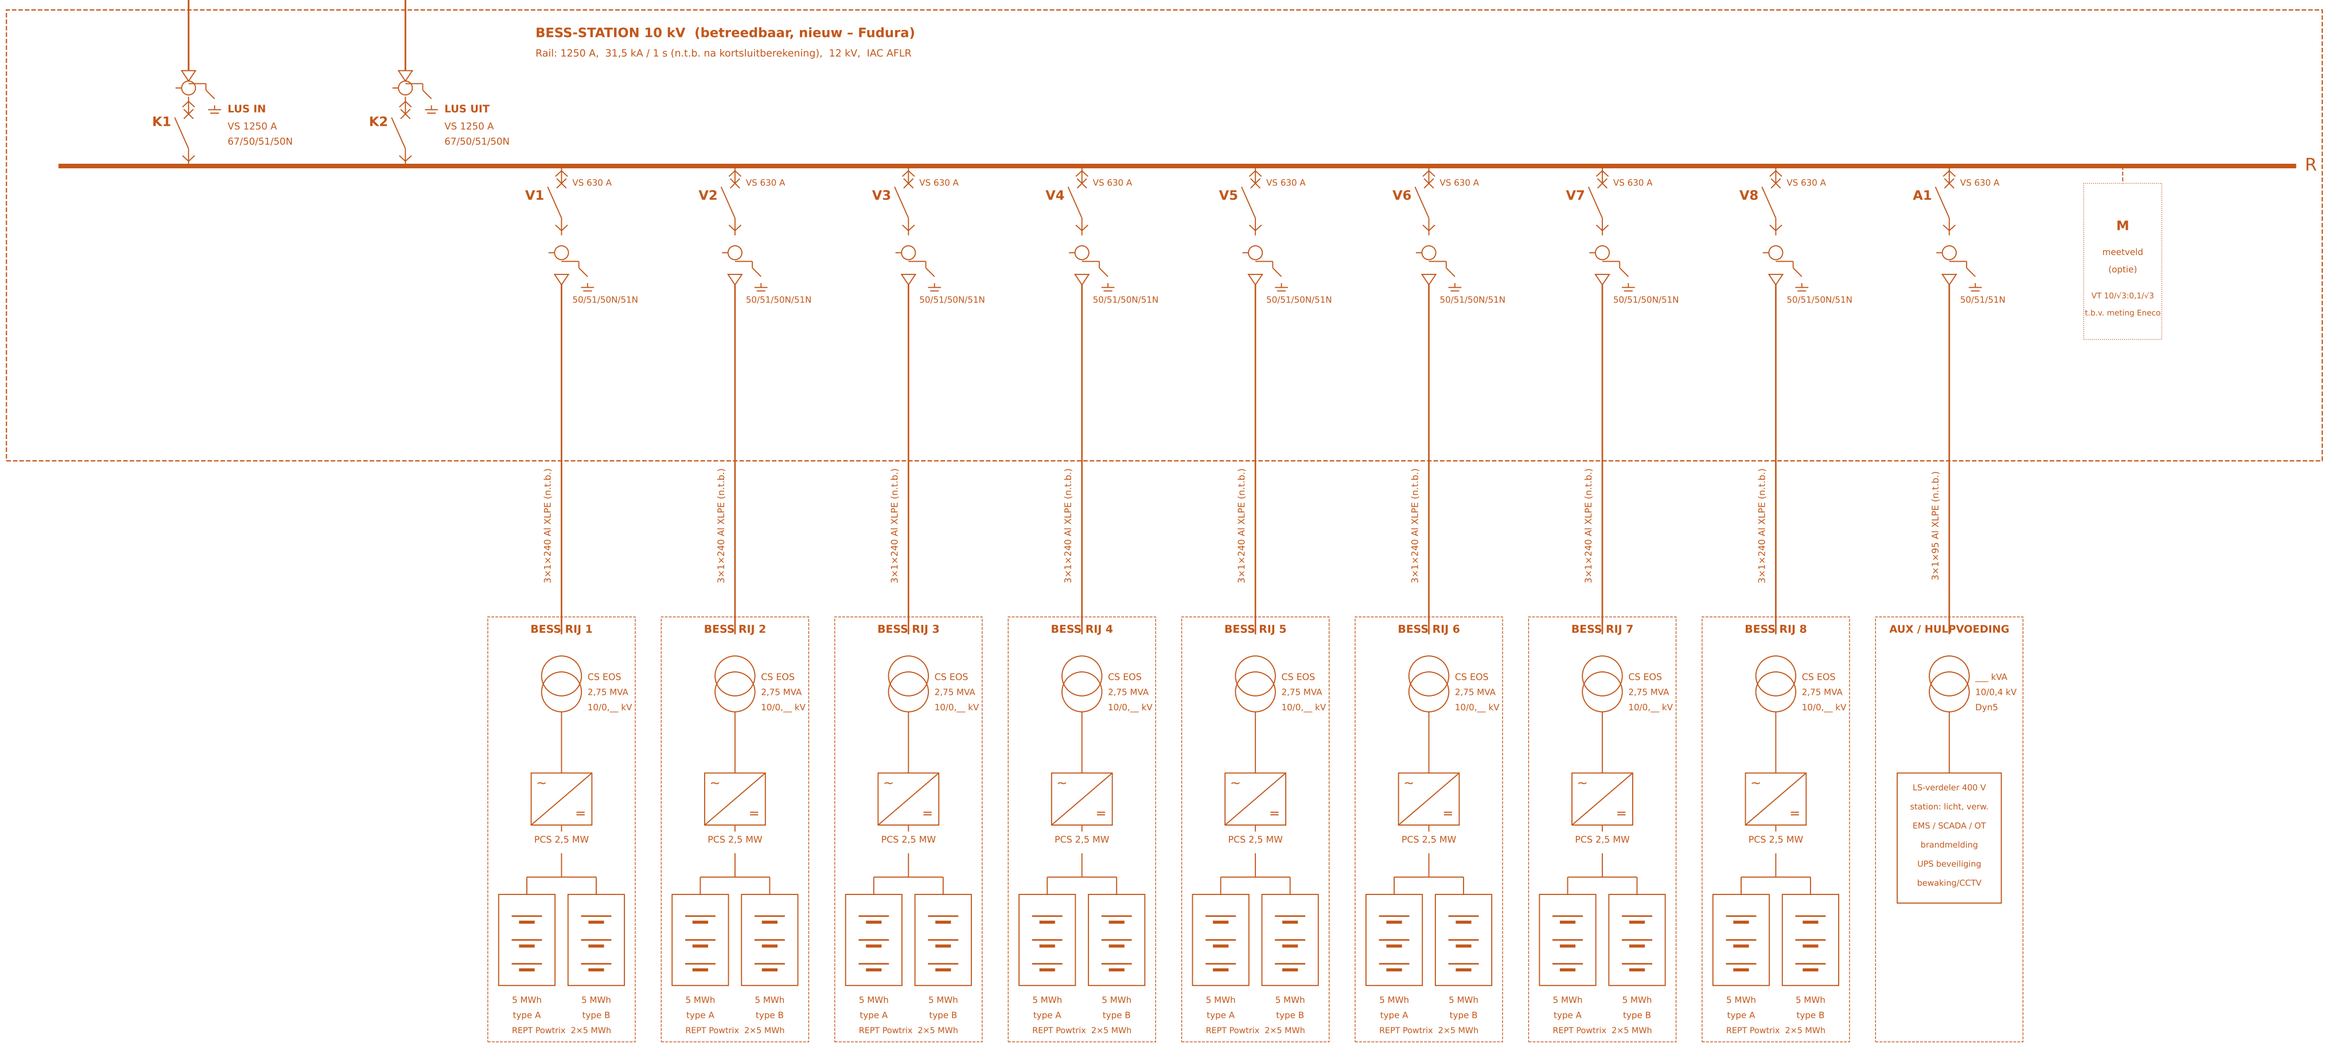

OPMERKINGEN / NOG TE BEPALEN

1. Aansluiting als lus op twee reserve velden C12 en C13 van HSS rail C (MMS/Eaton, 31,5 kA/3 s). Beide velden op dezelfde rail; nominale stroom en beveiliging van C12/C13 verifiëren bij Getec.
2. Lus dimensioneren op N-1: één streng moet volle 20 MW kunnen voeren (≈ 1155 A bij 10 kV). Kabel en VS K1/K2 1250 A; doorsnede na kabelberekening (Kablix).
3. Kortsluitvastheid: bijdrage BESS (8 × PCS) ≈ 1,2–1,7 kA + PV ≈ 0,2 kA bovenop bestaand; toetsen rail C (31,5 kA/3 s) en onderstations. Benodigd: Sk'' 110 kV, uk EGD1/2, x''d GEN1/2/3/6, X van L1–L4, L11–L13.
4. Netaarding Getec: halfster geaard via zig-zag-spoel. Aardfoutbeveiliging (50N/51N, evt. 67N) afstemmen op aardfoutstroom en uitschakeltijd van de spoel.
5. Per rij: CS EOS (trafo + LS) → PCS 2,5 MW (WSTECH APS) → 2 × REPT 5 MWh (type A + type B, rug-aan-rug alleen met brandtestrapport, PGS 37-1). Totaal 20 MW / 80 MWh.
6. Beveiligingsconcept, selectiviteit en instelwaarden volgen uit netstudie (Vision). Hulpspanning station 110 V DC (n.t.b.).

FUDURA Engineering MS/LS		
Getec Park.Emmen – BESS 20 MW / 80 MWh		
Eénlijnschema 10 kV – BESS-station en aansluiting HSS C12/C13 Status: CONCEPT – ter bespreking met Getec		
Getekend N. Cambeen	Datum / rev. 02-11-2026 rev. A	Blad / formaat 2 / 2 A2
Ref. Getec A0-0.673.581		