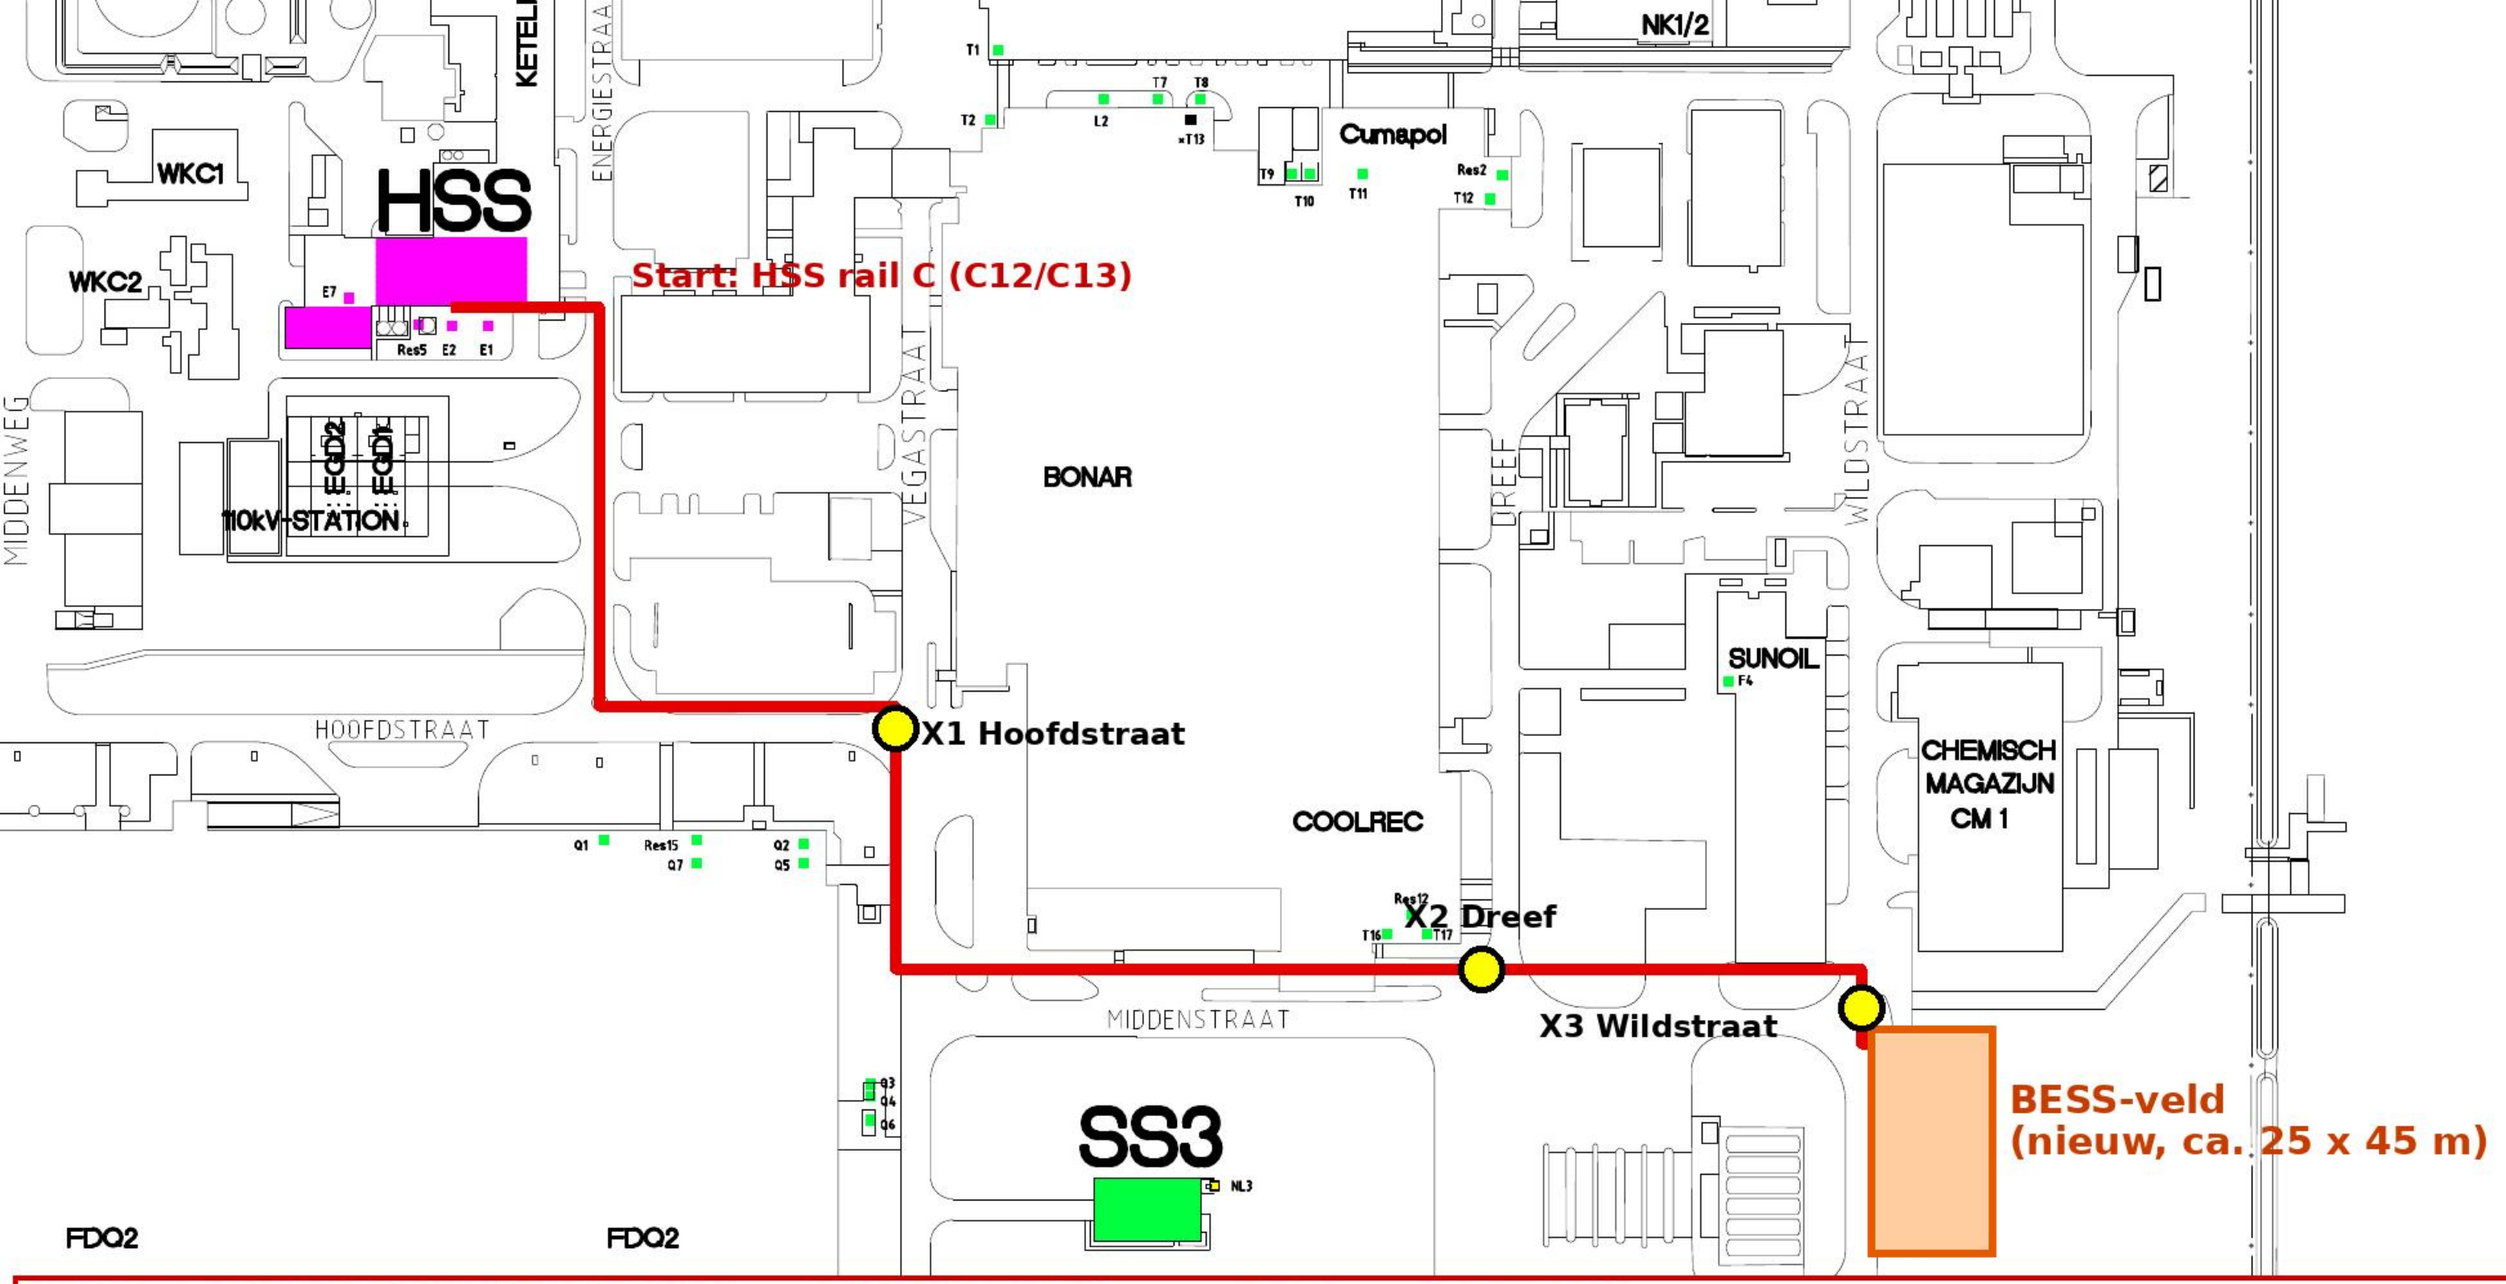


INDICATIEF KABELTRACÉ HSS C12/C13 -> BESS-STATION (concept Fudura, 4-11-2026)

Ondergrond: Getec tekening 000_Trafos_Terrein 0683330 blad 1. Positie BESS uit 3D-model/BAG (±30 m).

Tracé (rood) in de bermen langs Hoofdstraat, Vegastraat en Middenstraat; wegkruisingen X1-X3 haaks, met mantelbuis of boring.

Lengte ca. 430 m + ca. 40 m reserve/invoer = ca. 470 m per streng; strengen K1 (C12) en K2 (C13) in dezelfde sleuf.

Te bevestigen: bestaande kabels/leidingen (E-Grondkabels, KLIC), eigendom bermen, exacte plek BESS en HSS-invoer.