

SITUATIE KABELTRACÉ 10 kV HSS rail C → BESS-station (schaal ca. 1:1800 op A3)

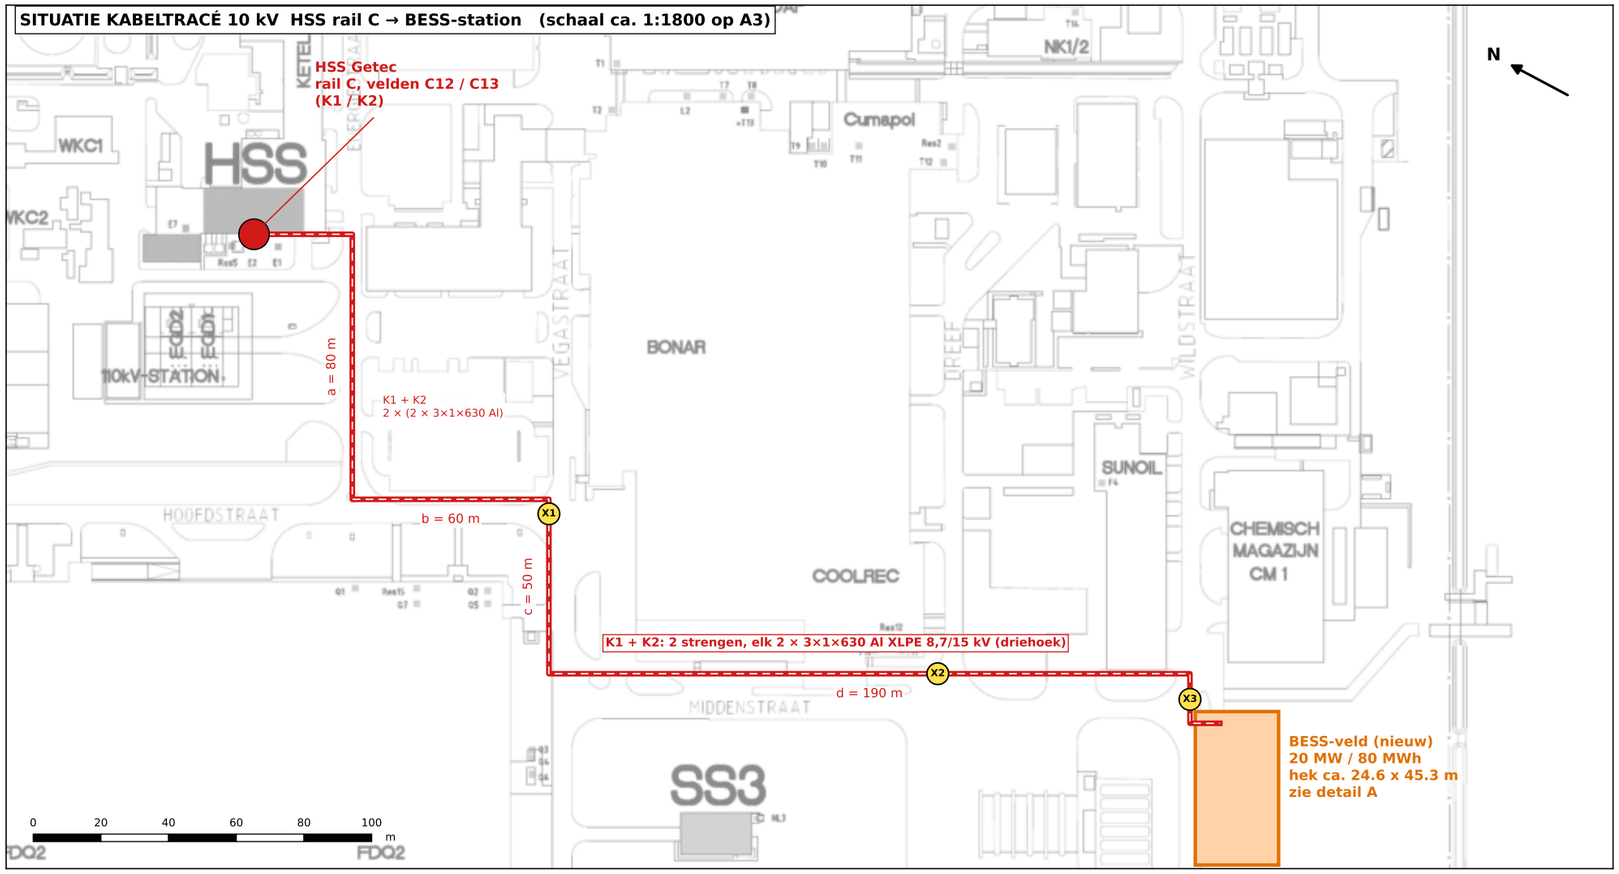

DETAIL A – BESS-veld (1:400 op A3)

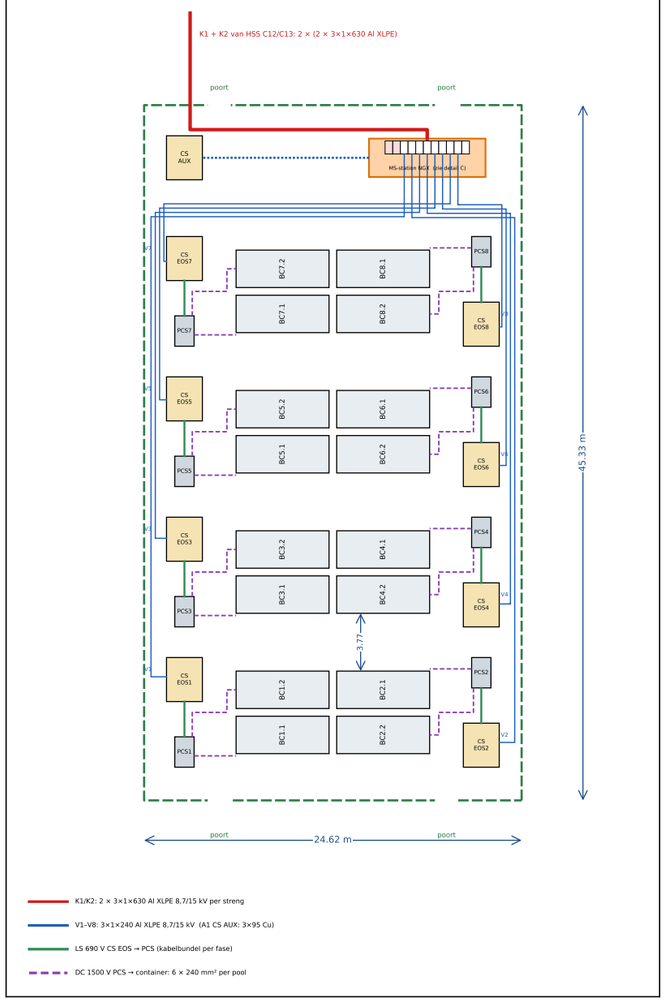


LEGENDA

- Nieuw MS-kabeltracé K1 + K2: 2 strengen in één sleuf, elk 2 × 3×1×630 Al XLPE 8,7/15 kV; a+b+c+d ≈ 430 m, met invoer en reserve ≈ 470 m per streng
- Nieuw BESS-veld: 8 × (CS EOS 2,5 MVA + PCS 2,5 MW + 2 × REPT 5 MWh), MS-station NGX 12 kV, CS AUX
- X — Kruising weg (X1 Hoofdstraat, X2 Dreef, X3 Wildstraat): haaks, mantelbuis of gestuurde boring
- Aansluitpunt bestaand: HSS Getec rail C, reservevelden C12 (K1) en C13 (K2)

OPMERKINGEN


1. Ondergrond: Getec-tekening 000_Trafos_Terrein 0683330 blad 1.
   Positie BESS-veld uit 3D-model / BAG, nauwkeurigheid ca. ±30 m.
2. Tracé in de bermen langs Hoofdstraat, Vegastraat en Middenstraat.
   Bestaande kabels en leidingen controleren (E-Grondkabels, KLIC).
3. Aansluiting HSS rail C (MMS/Eaton 31,5 kA): veldstroom ≥ 1250 A
   en beveiliging van C12/C13 verifiëren bij Getec.
4. Per streng 2 × 3×1×630 Al XLPE 8,7/15 kV (N-1: 1 streng = 20 MW,
   ca. 1155 A). Definitief na kabelberekening.
5. Lengtes a–d gemeten op de ondergrond; definitief na inmeting.

6. CONCEPT / INDICATIEF – NIET VOOR UITVOERING.

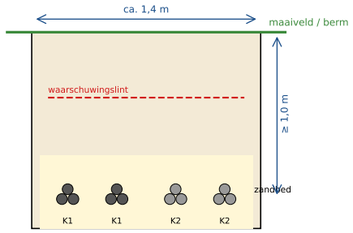

DETAIL B – sleufprofiel (indicatief): 4 × 3×1×630 Al XLPE in driehoek

DETAIL C – MS-station 10 kV, NGX 12 kV 25 kA/3 s: veldopstelling (vooraanzicht, indicatief)

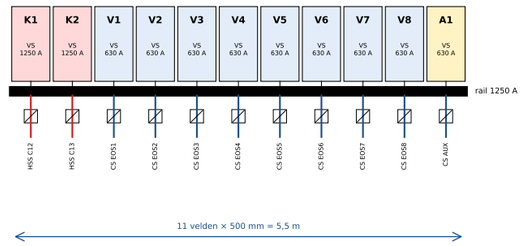

FUDURA

Engineering MS/LS – team PER

Project: Getec Park Emmen – BESS 20 MW / 80 MWh

Opdrachtgever: GETEC Park Emmen, Eerste Bokslootweg 17, Emmen

Situatie en indicatief kabeltracé 10 kV
HSS rail C (C12/C13) → BESS-station

Tekeningnr.	Revisie	Datum
FUD-GET-BESS-E-001	**A – CONCEPT**	**04-11-2026**
Getekend	Schaal	Formaat
N. Cambeen	**ca. 1:1800 / 1:400 (A3)**	**A3 liggend**